


RUNWAY/TAXIWAY/APRON PHYSICAL CHARACTERISTICS		
RWY / TWY / APRON	SURFACE	PCN
RWY 05/23	Grooved Asphalt	65/R/B/W/T
TWY A, B, D, E, F & G	Asphalt	-
TWY J	Asphalt	-
TWY T	Asphalt	-
TWY W	Concrete	-
TWY Y	Concrete/Asphalt	-
TWY Z	Concrete/Asphalt	-
Apron (All)	See AD 2-EGPF-2-2	

GUND (Geoid Undulation) = The height of the Geoid (MSL) above the Reference Ellipsoid (WGS 84) at the stated position.	
BEARINGS ARE MAGNETIC ELEVATIONS AND HEIGHTS ARE IN FEET	
ELEVATIONS IN FEET AMSL	72 (46)
HEIGHTS IN FEET ABOVE AD	

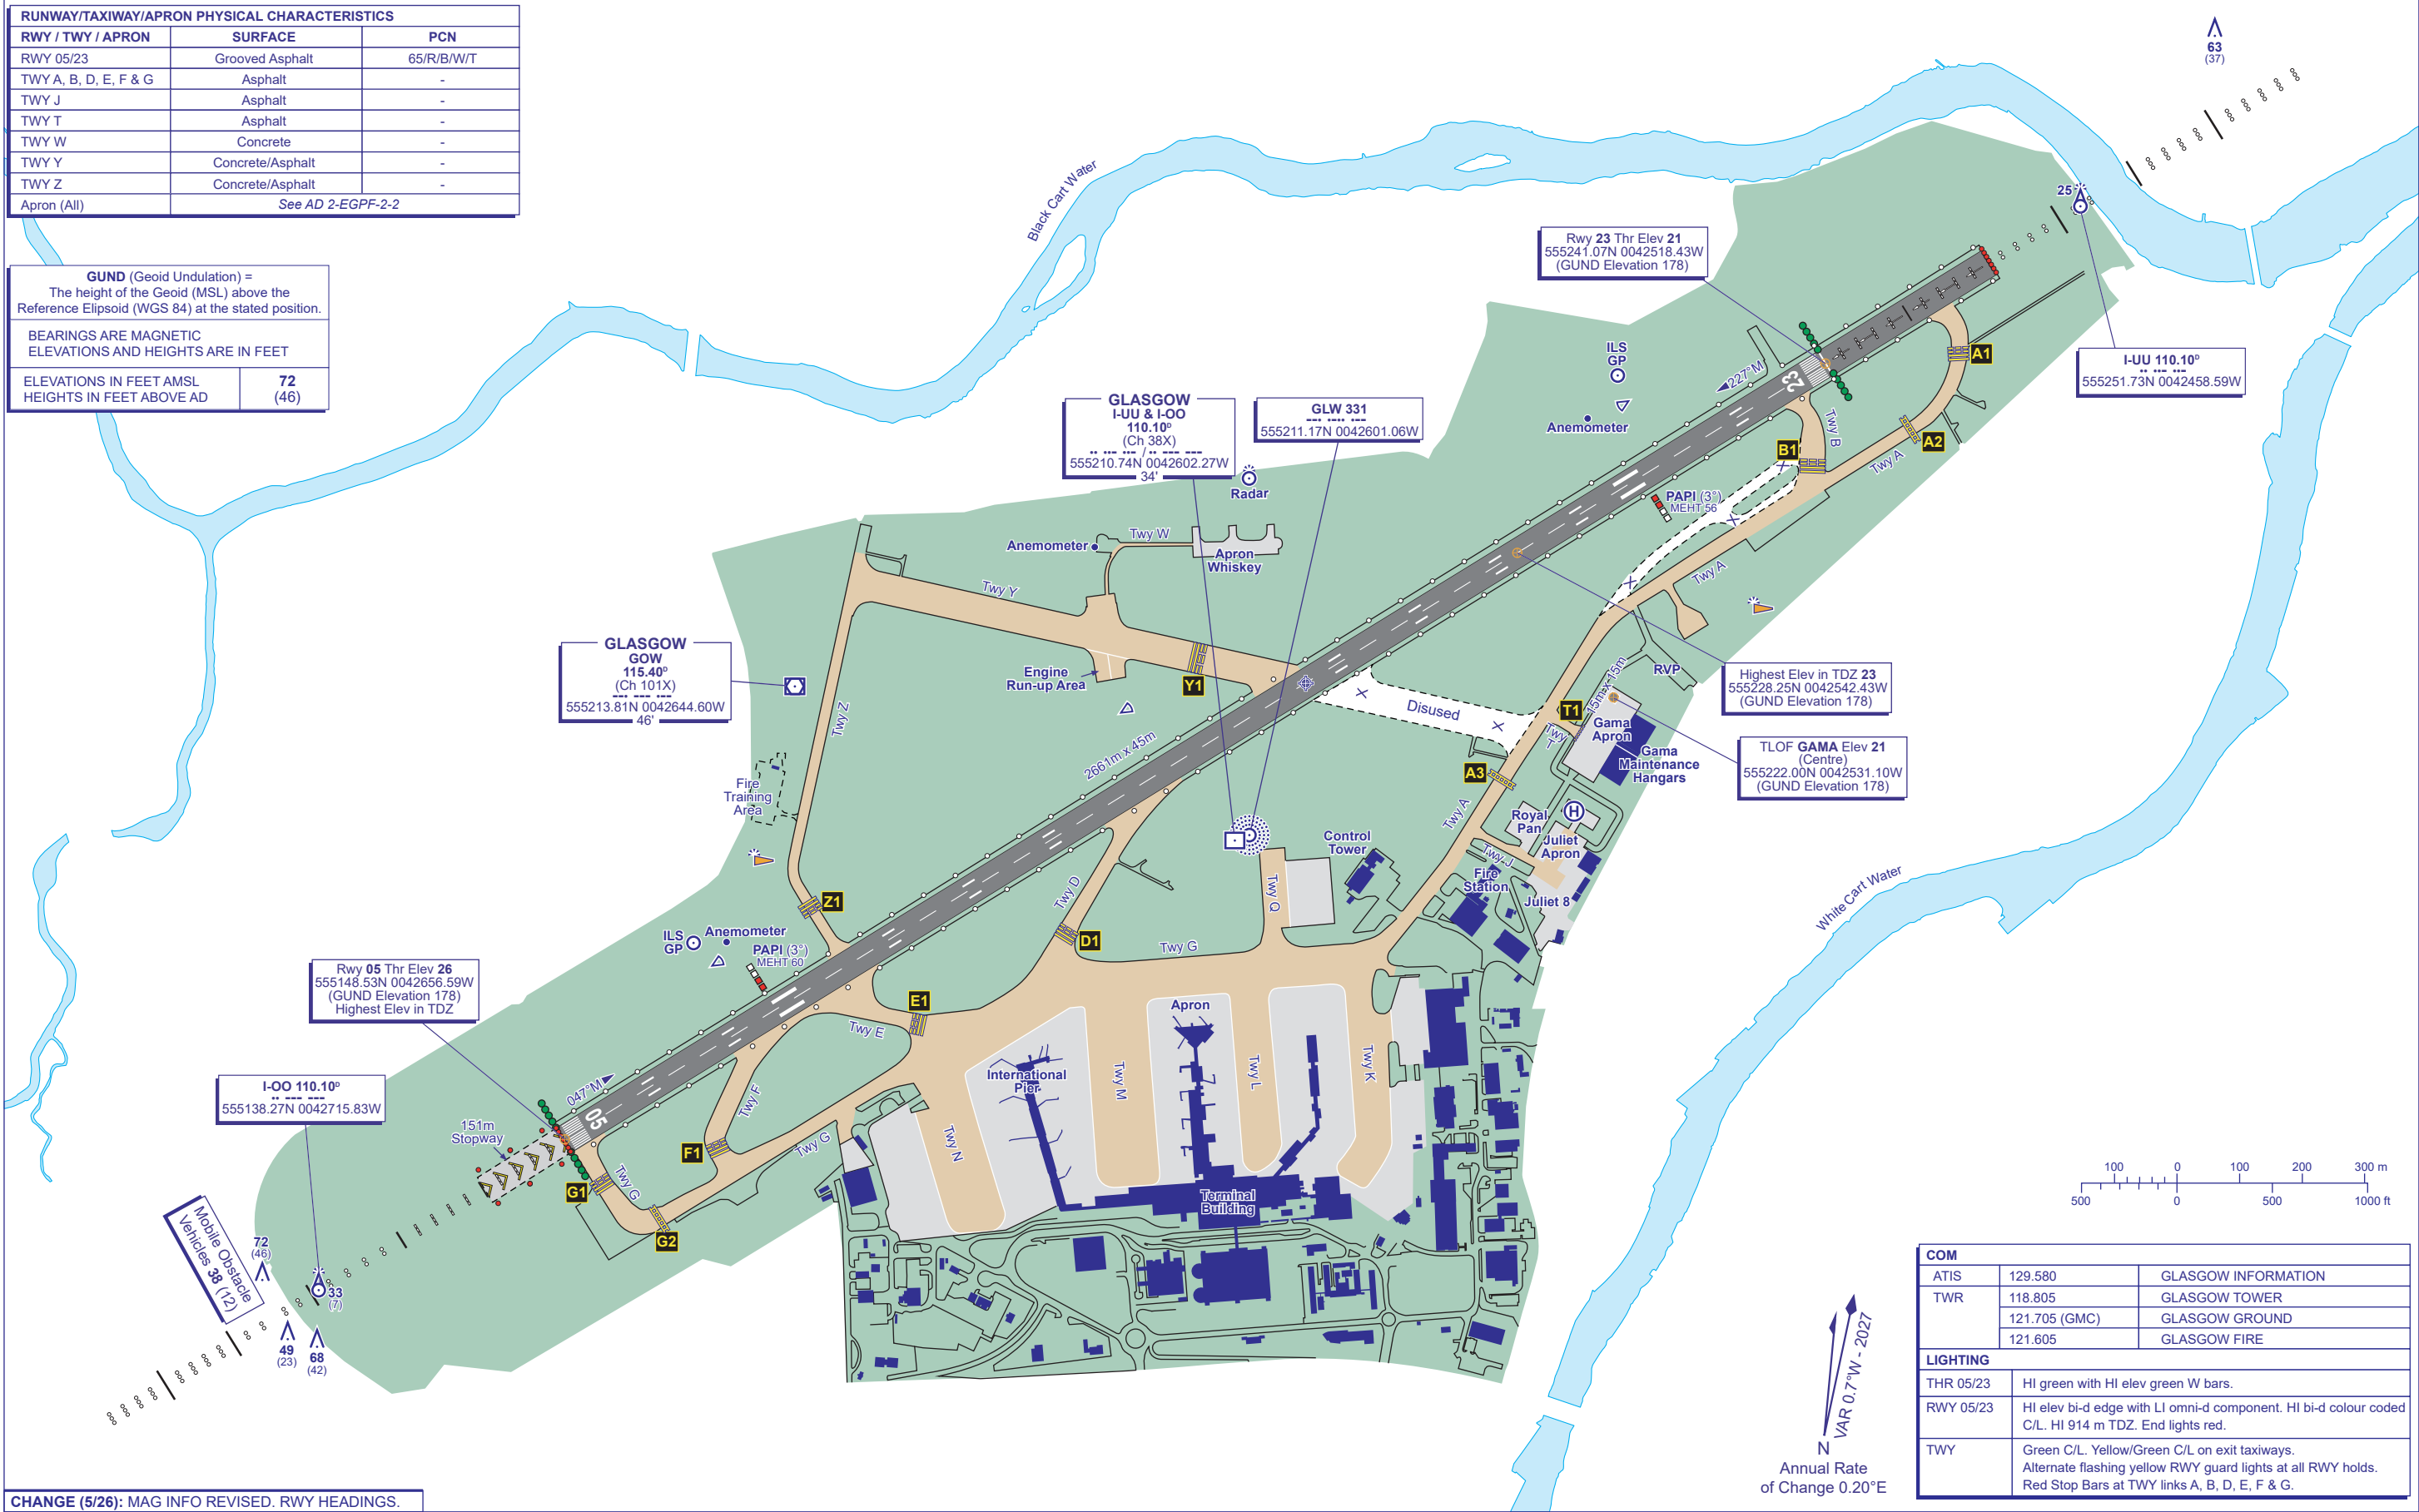

CHANGE (5/26): MAG INFO REVISED. RWY HEADINGS.

AERO INFO DATE 18 FEB 26

COM		
ATIS	129.580	GLASGOW INFORMATION
TWR	118.805	GLASGOW TOWER
	121.705 (GMC)	GLASGOW GROUND
	121.605	GLASGOW FIRE
LIGHTING		
THR 05/23	HI green with HI elev green W bars.	
RWY 05/23	HI elev bi-d edge with LI omni-d component. HI bi-d colour coded C/L. HI 914 m TDZ. End lights red.	
TWY	Green C/L. Yellow/Green C/L on exit taxiways. Alternate flashing yellow RWY guard lights at all RWY holds. Red Stop Bars at TWY links A, B, D, E, F & G.	

AD 2-EGPF-2-1